


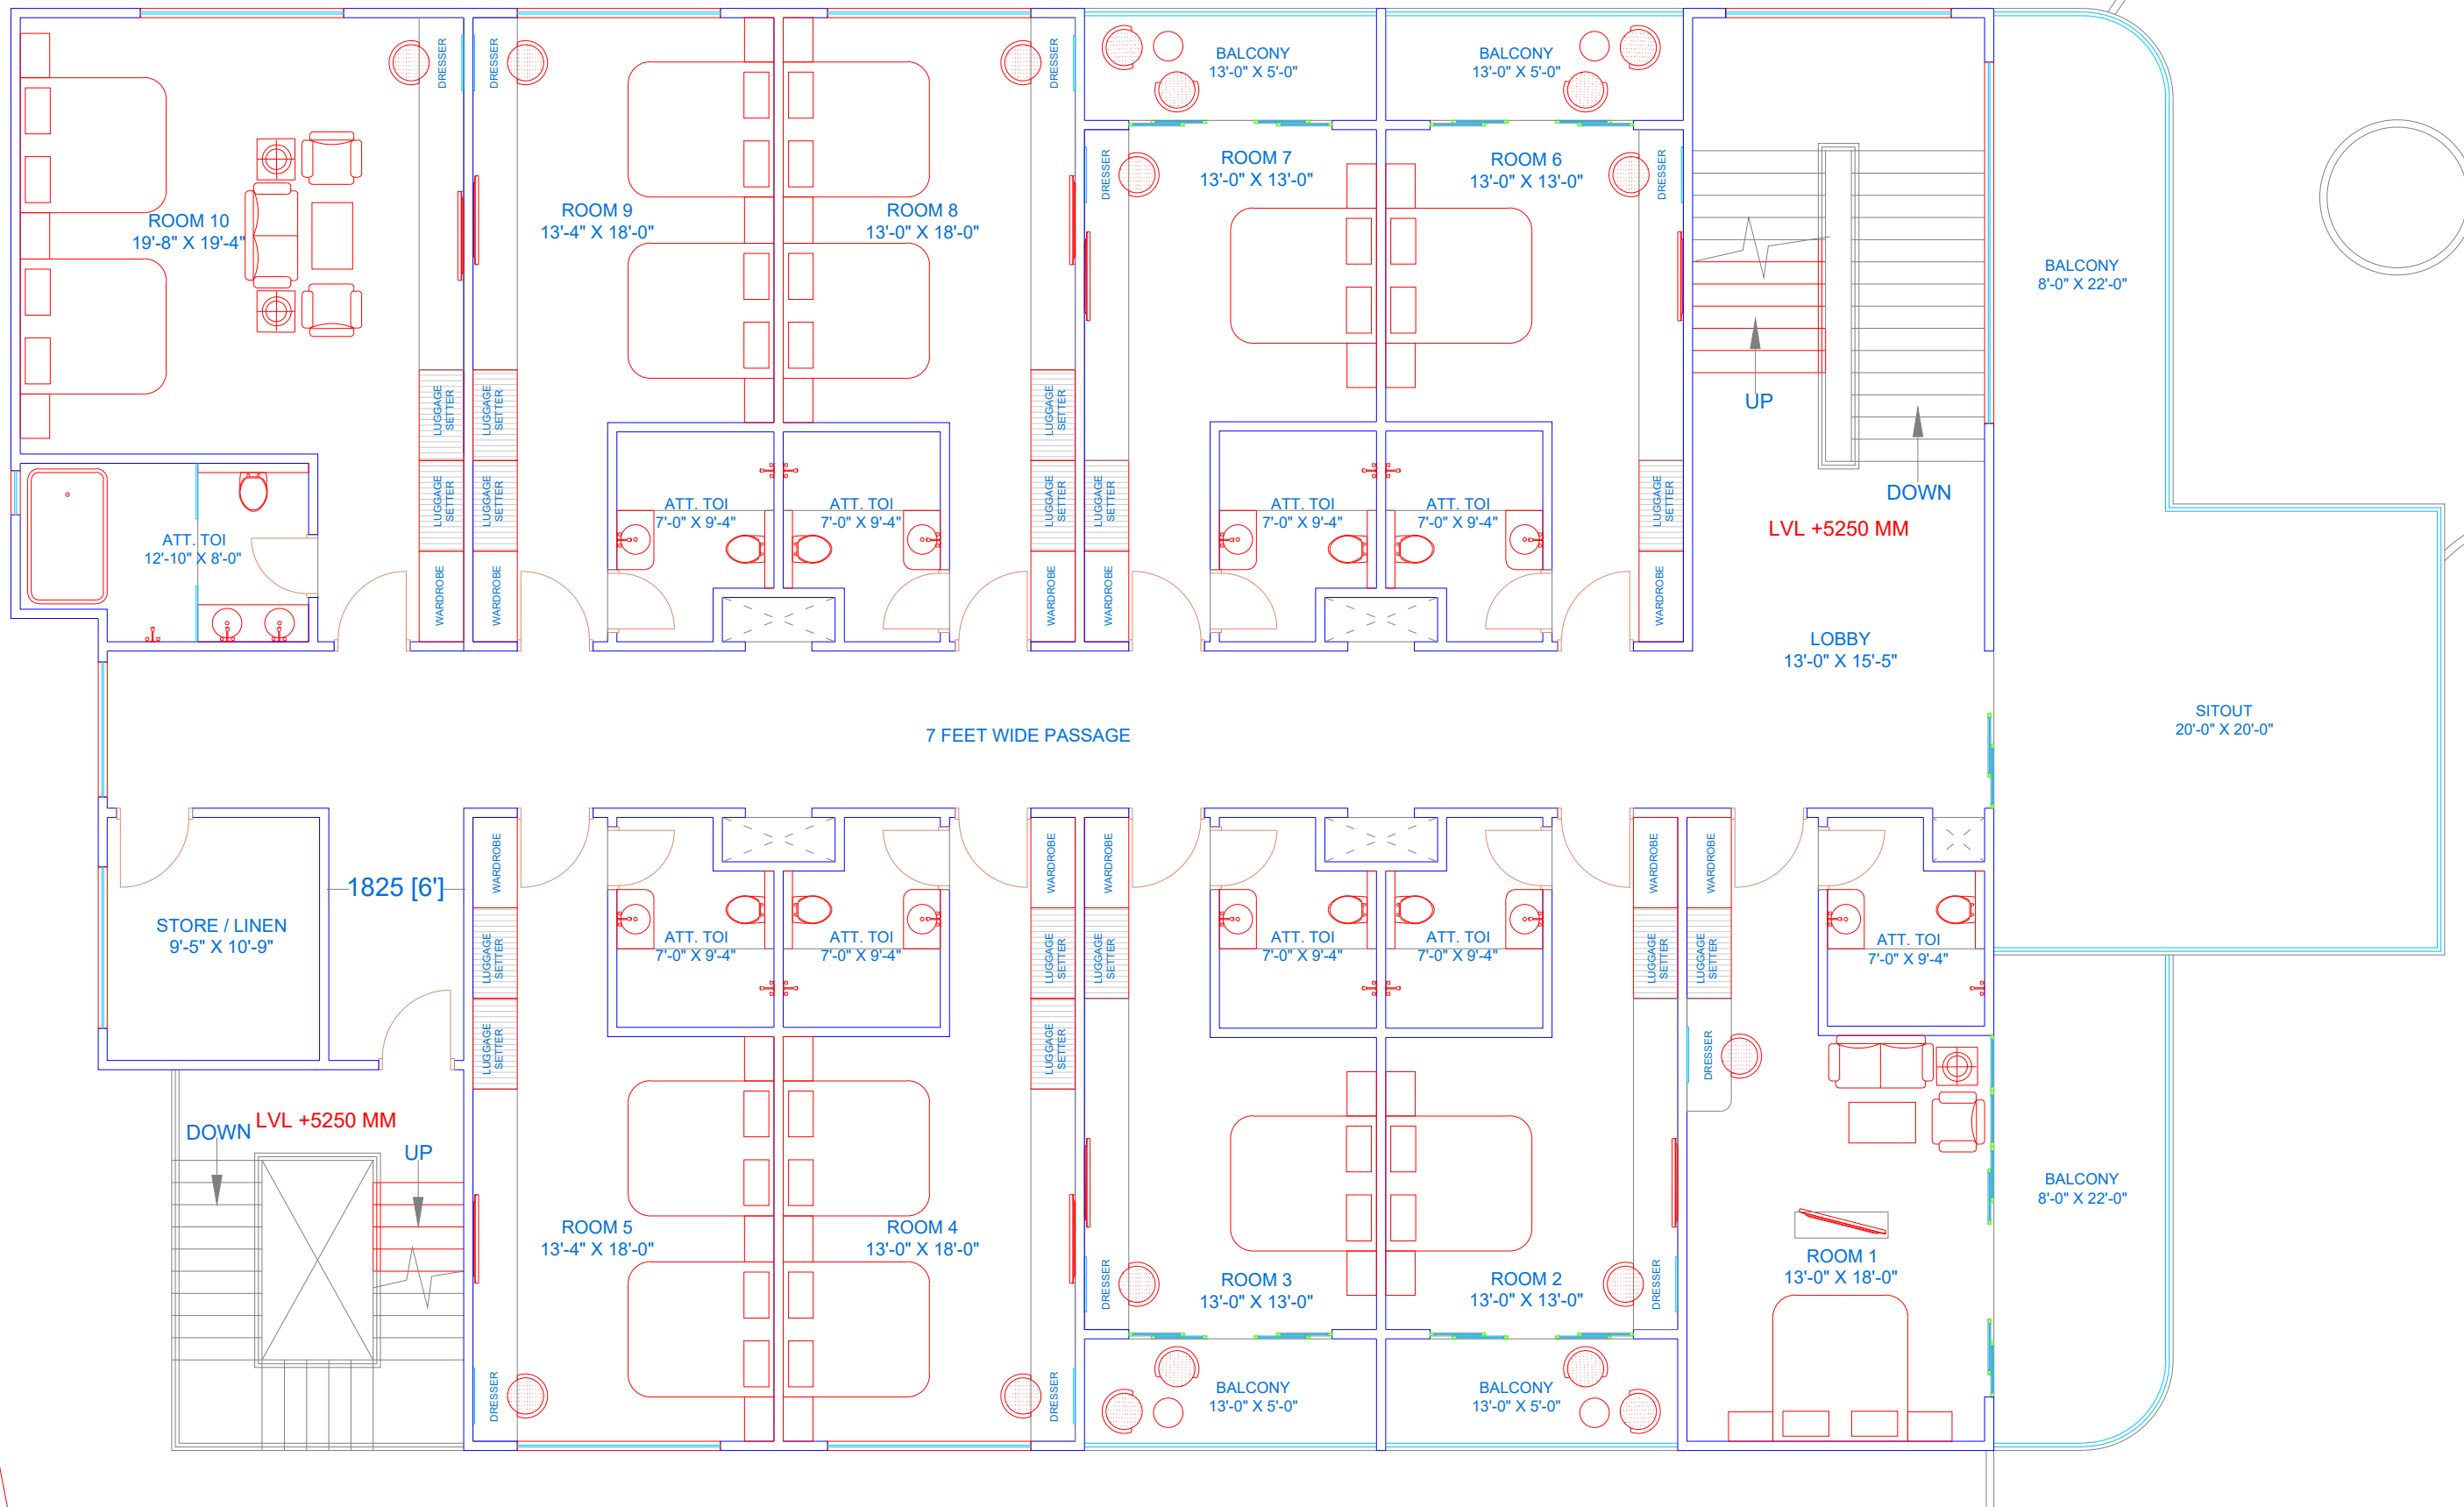

TITLE: FIRST FLOOR PLAN.

CLIENT: MR. CHETAN JI.

PROJECT NAME:
G+2 RESORT AT KATIHAR.

DESIGNED BY :
AR. PUJA AGARWAL

SIGN.

CHECKED BY :
ID. KAVITA MUNDRA

SIGN.

SCALE = N.T.S


SHEET NO: 02

REV. NO. : 01

DATE - 02.06.2026

SIGN OF ENGINEER

SIGN.

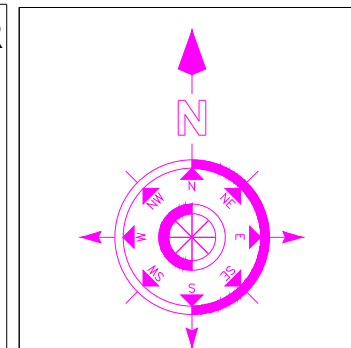



K M B D

ARCHITECT & ENGINEERS CONSORTIUM PVT.LTD
5TH FLOOR, DWARIKA ELEGANCE, BURDWAN ROAD,
RK COMPOUND, SILIGURI-734005,
PH.NO.- 2540737 (O), 9434047719 (M)
E-MAIL: kmbdsiliguri@gmail.com,
Our Website: www.kmbd.in

THIS DRAWING IS THE PROPERTY OF KMBD AND WILL NOT BE USED FOR ANY PURPOSE OTHER THAN SPECIFIED WITHOUT THEIR PRIOR WRITTEN PERMISSION.